

MATERIAL LISTE ELEKTRO

KIR ROHR M20 + BRIDEN	100m	Waco klemmen 3er/5er 200Stk 100Stk
--------------------------	------	--

DÖSEN T13 2fach 17 15 Stk	1mal geschaltet
---	-----------------

Dosen T13 2fach 15 Stk	Schrauben
---------------------------	-----------

Schalter S3 2fach 2 Stk	Schalter	Wachsmaschine last? ein Sicherheit? Boiler maße? ?
----------------------------	----------	---

Schaltw S3/S0 4 Stk	Cafer Bad Durchgang	direkt angeschlossen Kabel Schalteranschlussdose
------------------------	---------------------	--

1 Dose Außen 3 x T13
Nass

Außen
Steckdose


Abzweigboxen nicht zu klein
20 Stk

8 LAMPEN
3 Decke
1 Außen


T dreht
Erde grün/gelb
Null blau
Phase braun

gedr. Phase weiss
orange
schema 3 rosa/hellgrün


BAD
LAGER
BÜRO

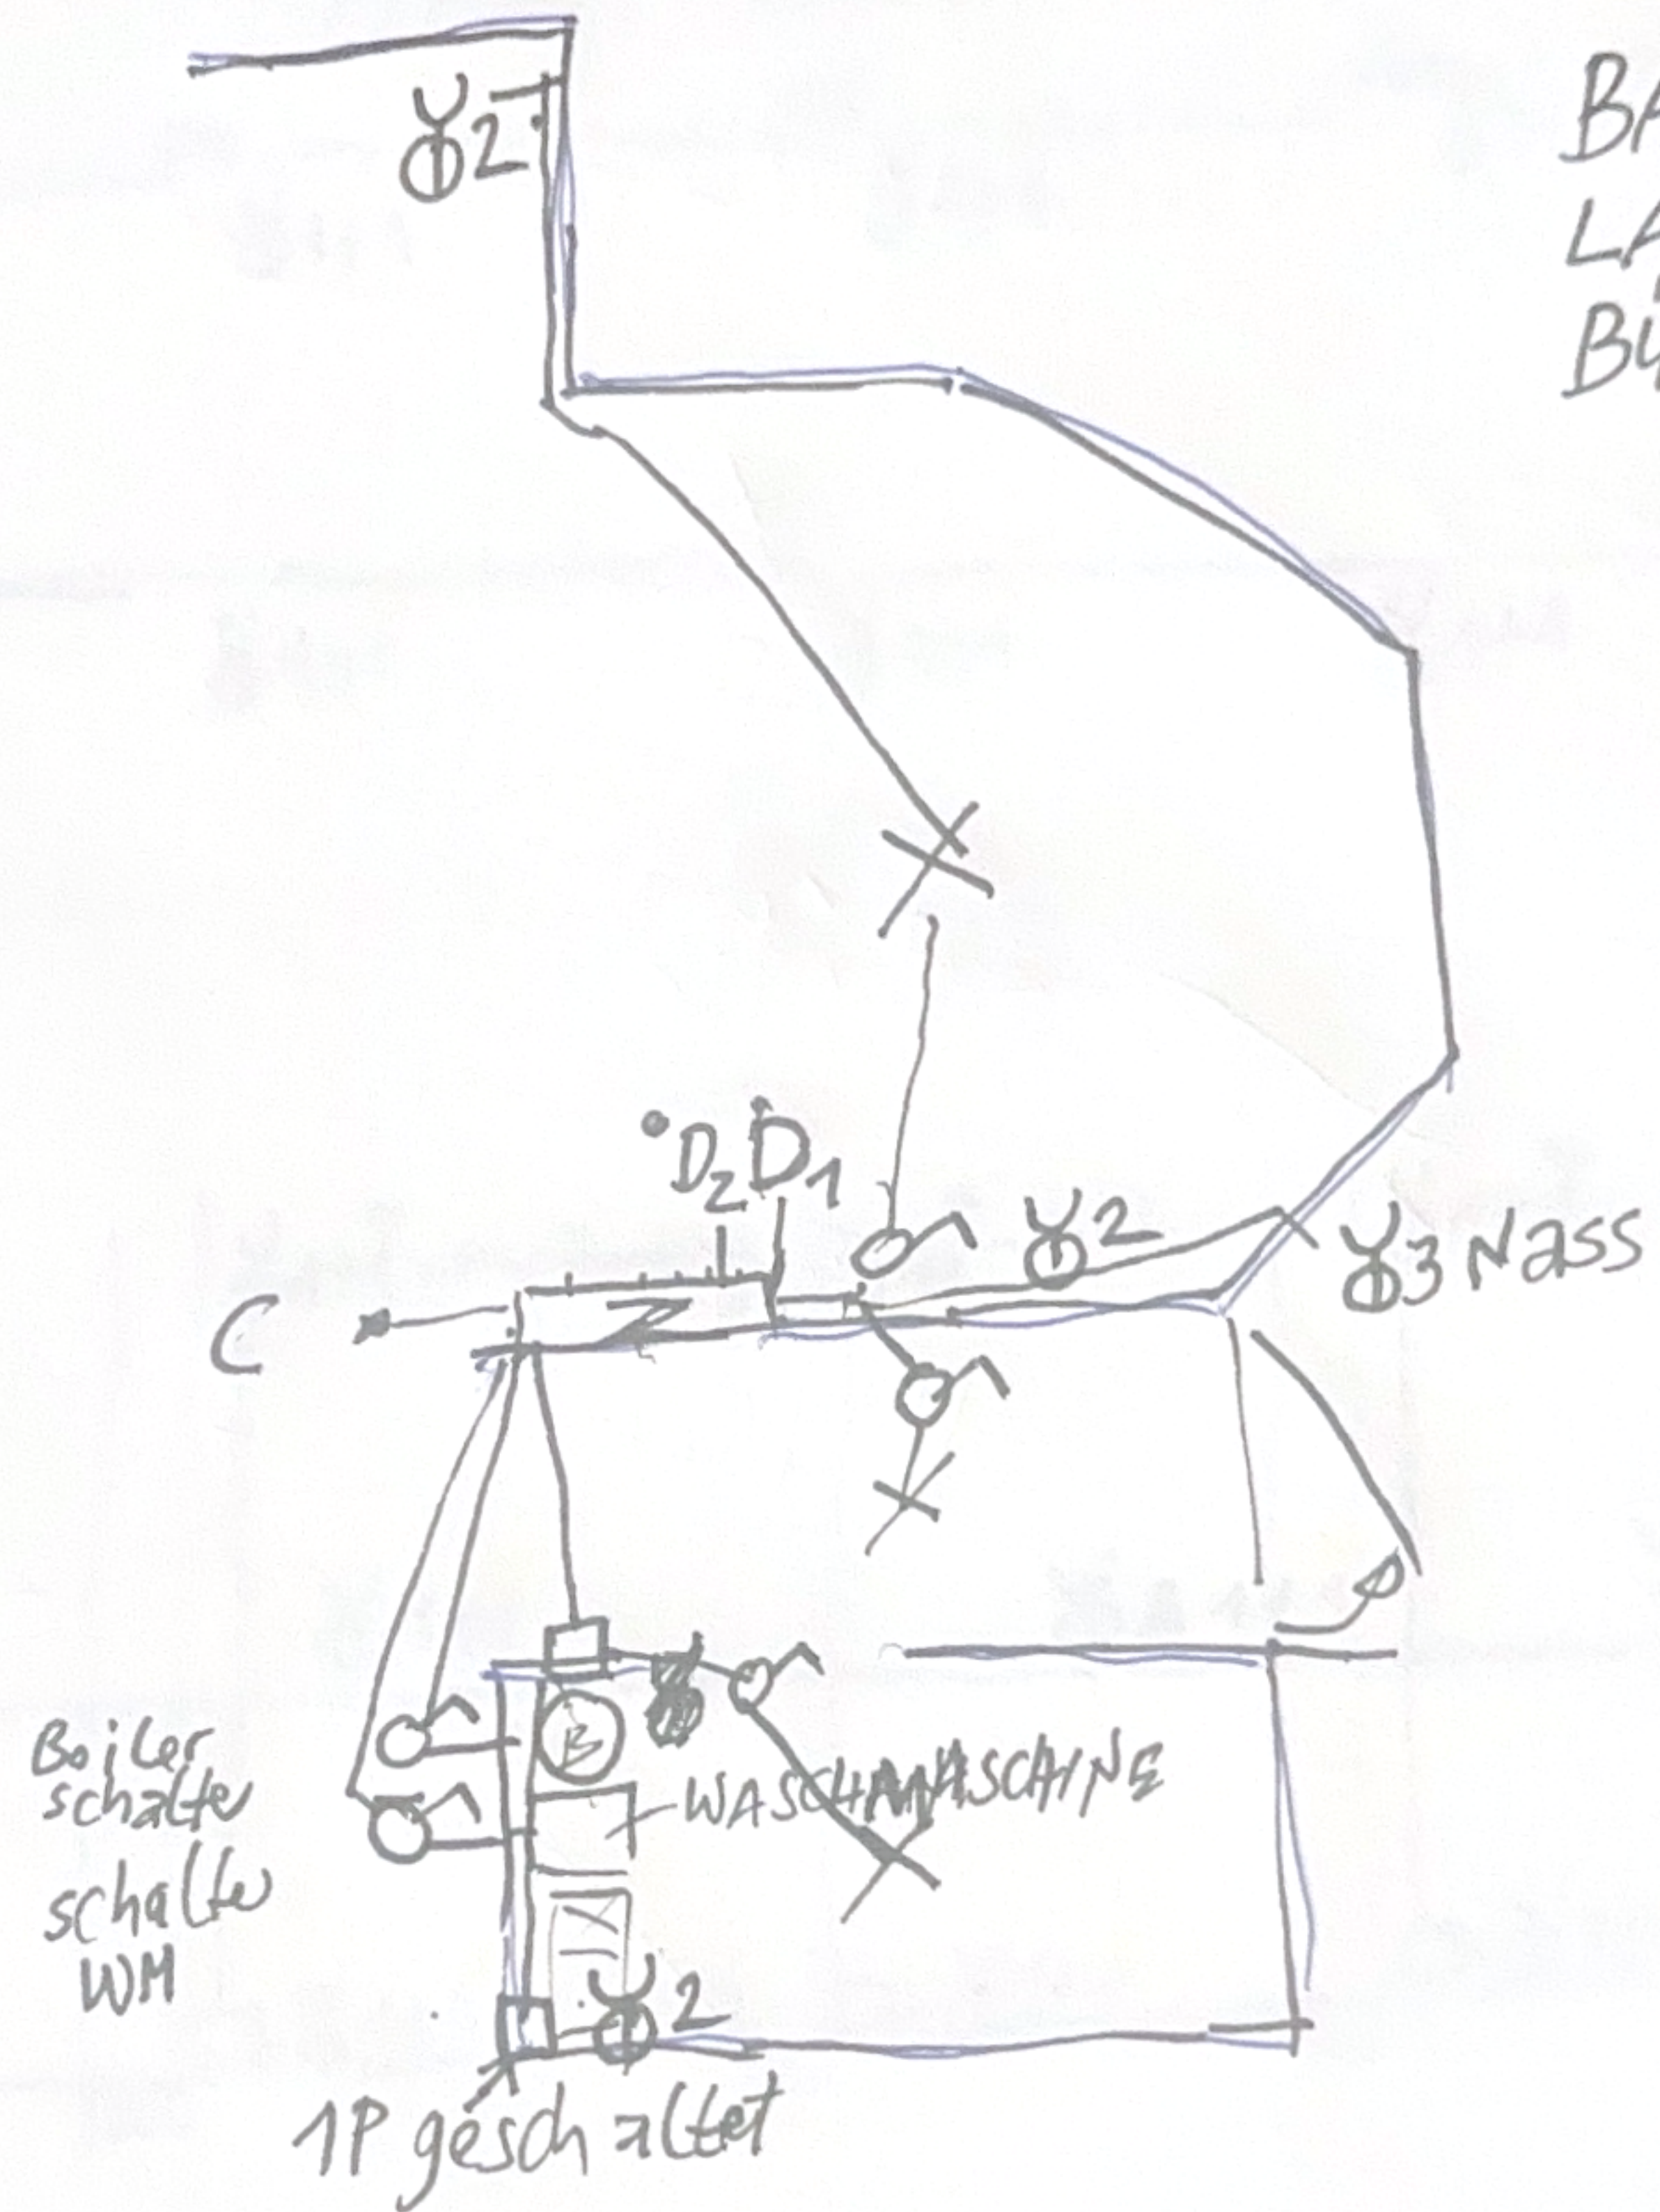

HAUPTRAUM

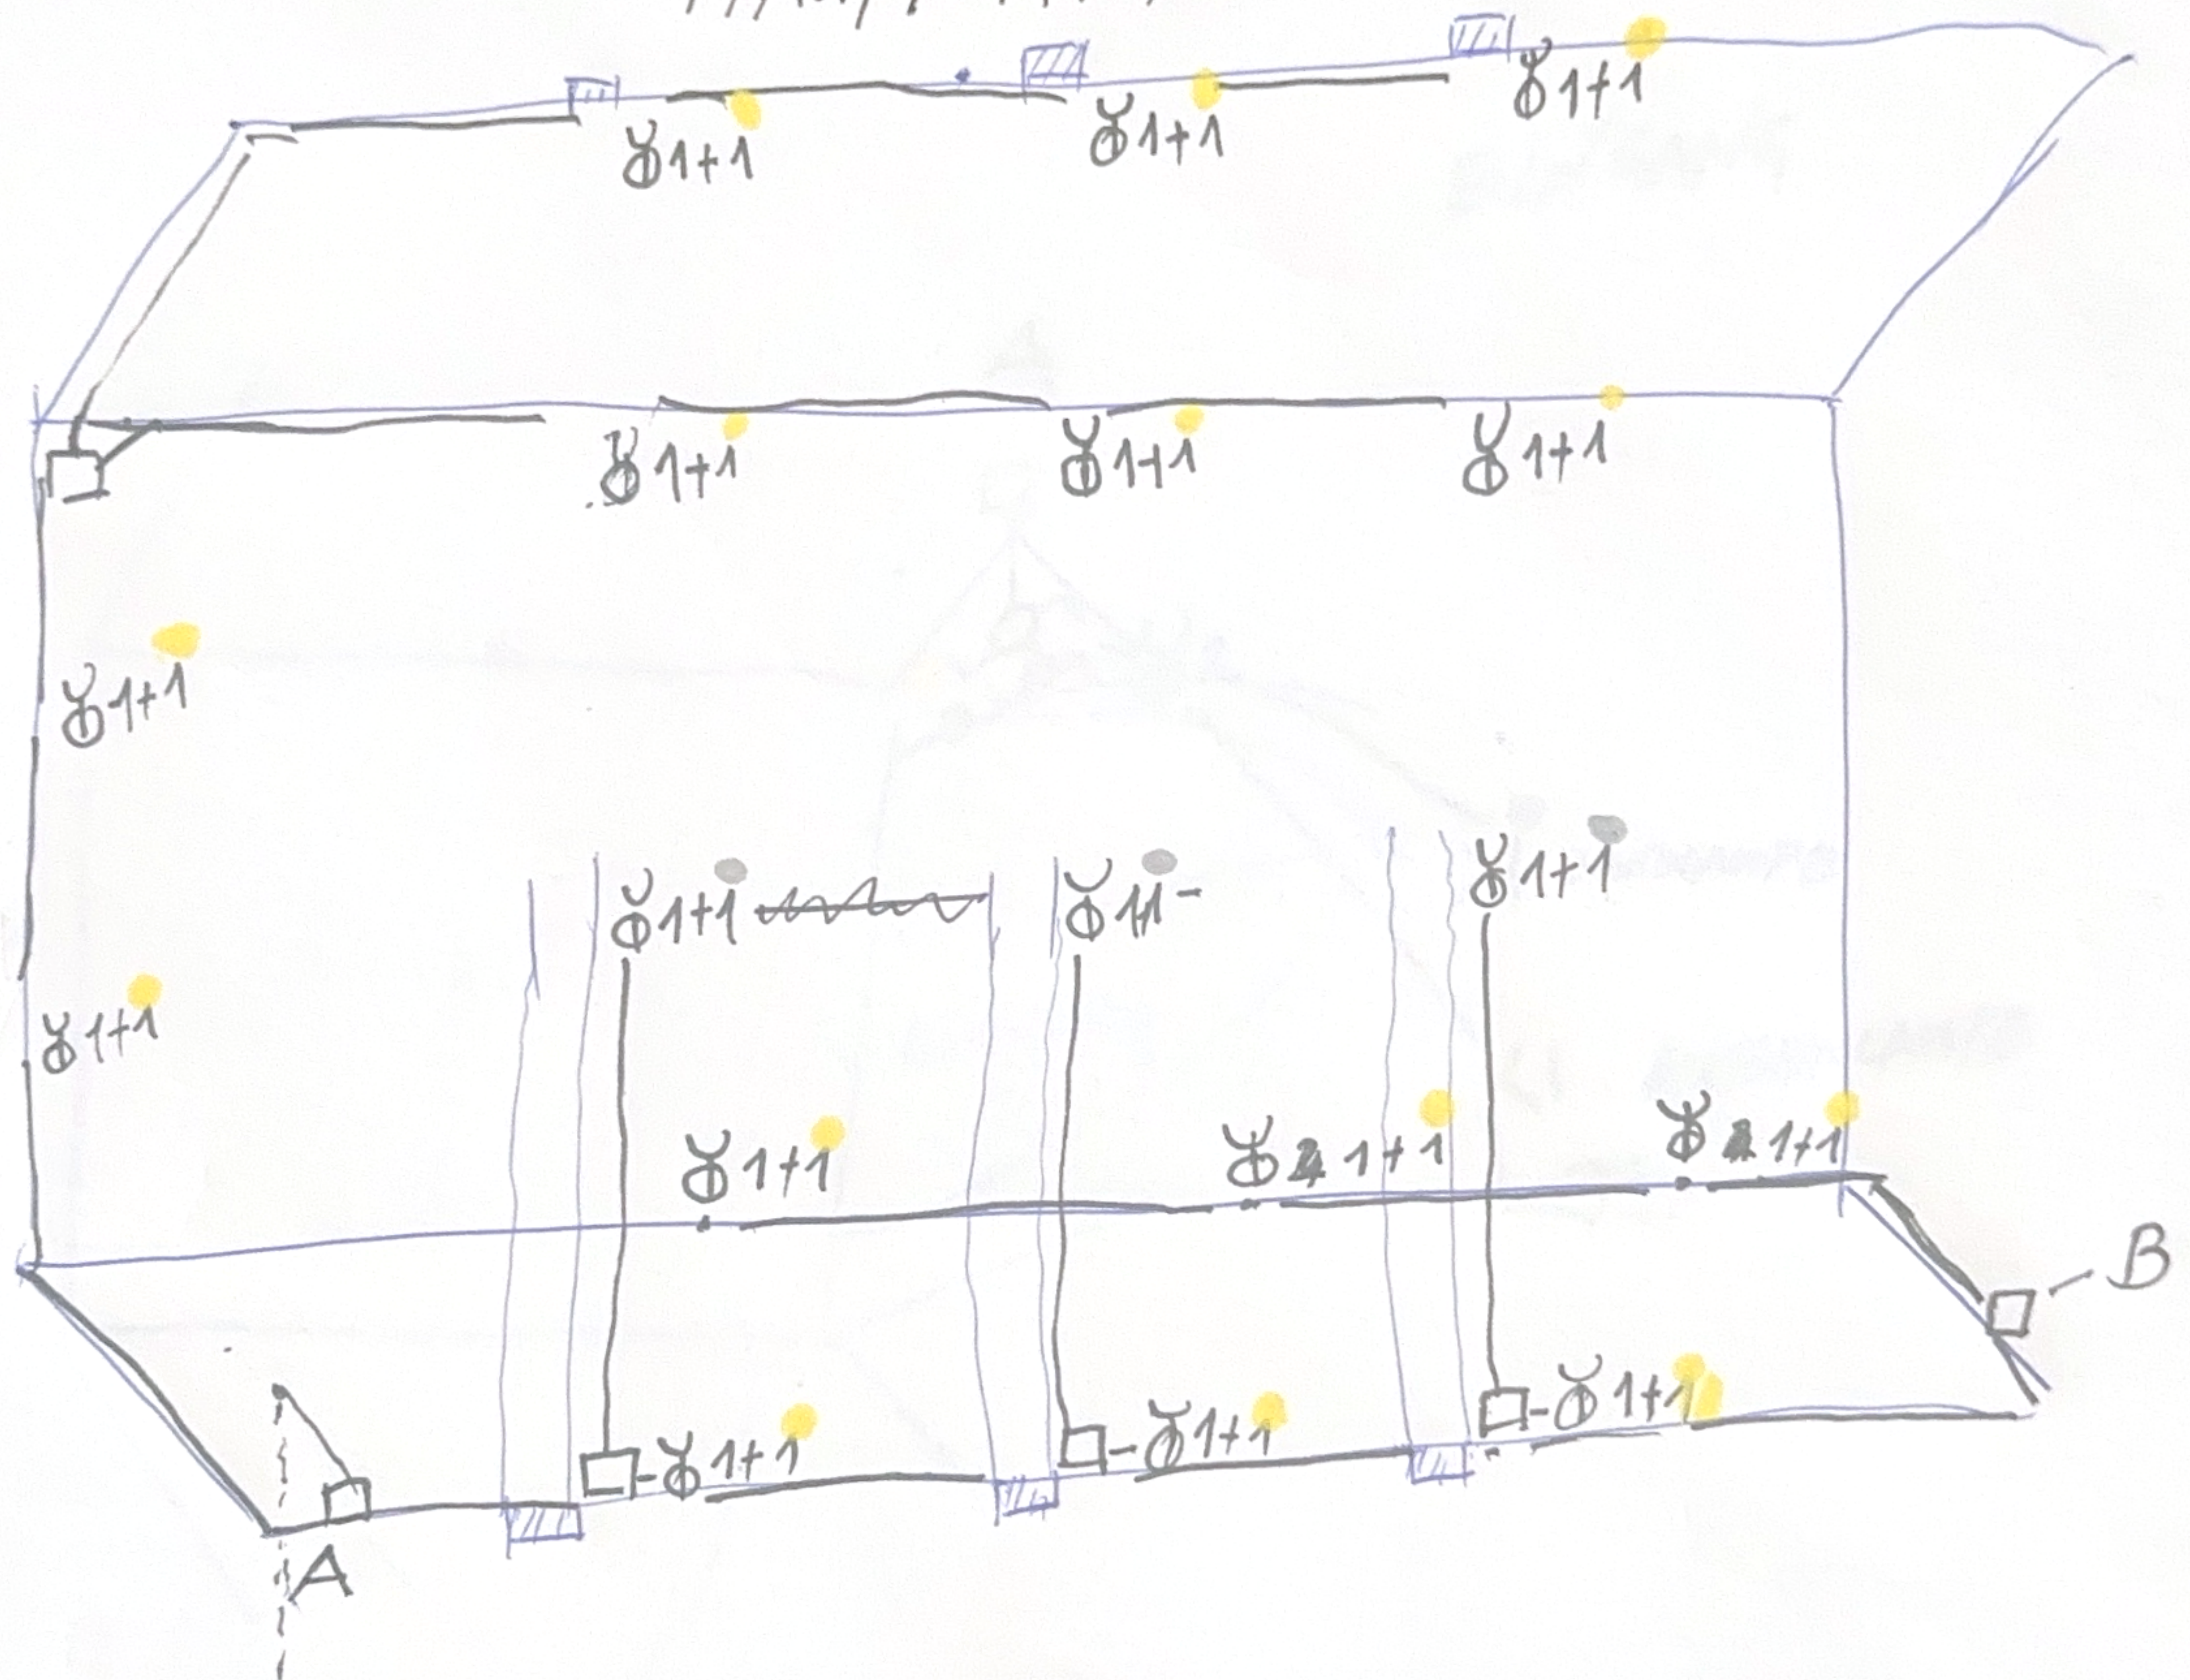

EINGANG

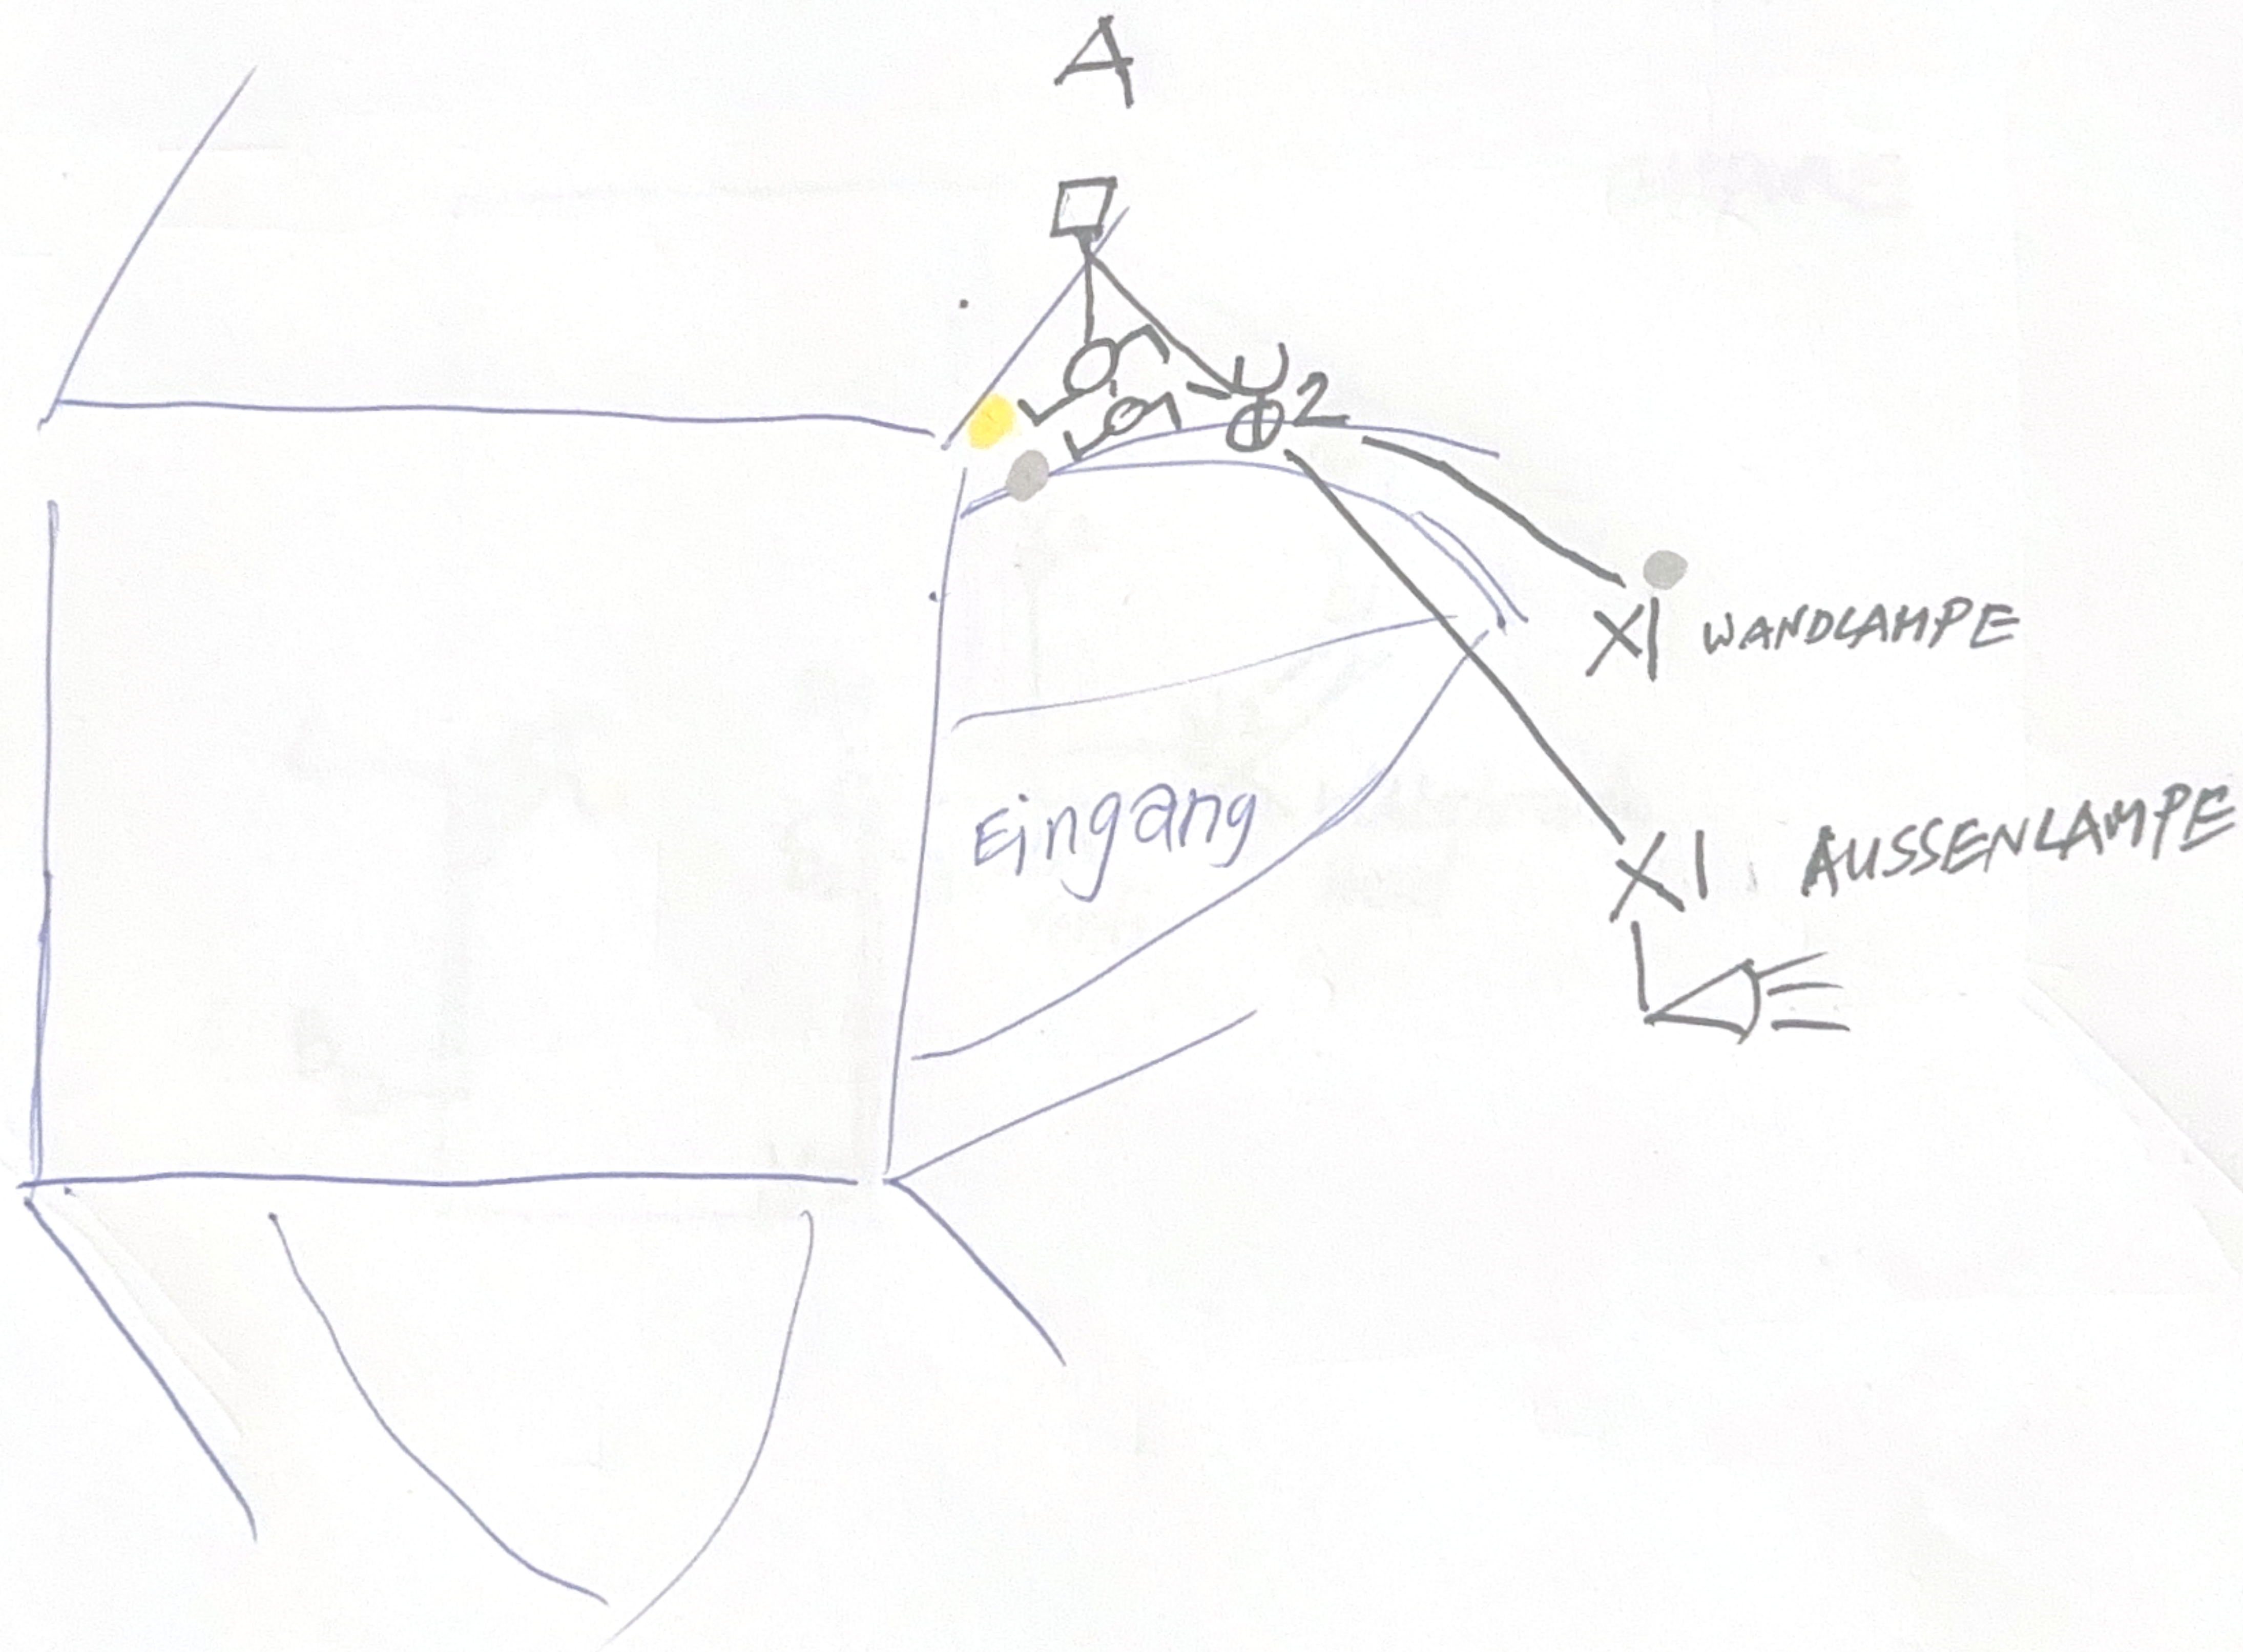

EYPORE

